




TEMPLE DRAWINGS

REVISIONS			This drawing is the property of Pradeep Sachdeva Design Associates and may not be used without written consent. Do not scale off this drawing, use figured dimensions only. Verify all dimensions at site.	ARCHITECT PRADEEP SACHDEVA DESIGN ASSOCIATES 4,Windmill Place, Ayanagar Village, New Delhi 110047 Ph:(011)26503741/ 9810054675 , e mail : design@ayanagar.com	PROJECT			TITLE : New column details		SHEET NO.	
Date	No	Descriptions			TEMPLE IN ORISSA			DATE : 5-11-2025		Revision no.	
					CLIENT			Scale : 3"=4'-0"(A3)			



REVISIONS			This drawing is the property of Pradeep Sachdeva Design Associates and may not be used without written consent. Do not scale off this drawing, use figured dimensions only. Verify all dimensions at site.	ARCHITECT PRADEEP SACHDEVA DESIGN ASSOCIATES 4, Windmill Place, Ayanagar Village, New Delhi 110047 Ph: (011) 26503741 / 9810054675, e mail : design@ayanagar.com	PROJECT TEMPLE IN ORISSA CLIENT			TITLE : Plan and Elevation	SHEET NO.
Date	No	Descriptions						DATE : 9-10-2025	Revision no.
								Scale : 1"=8'-0"	

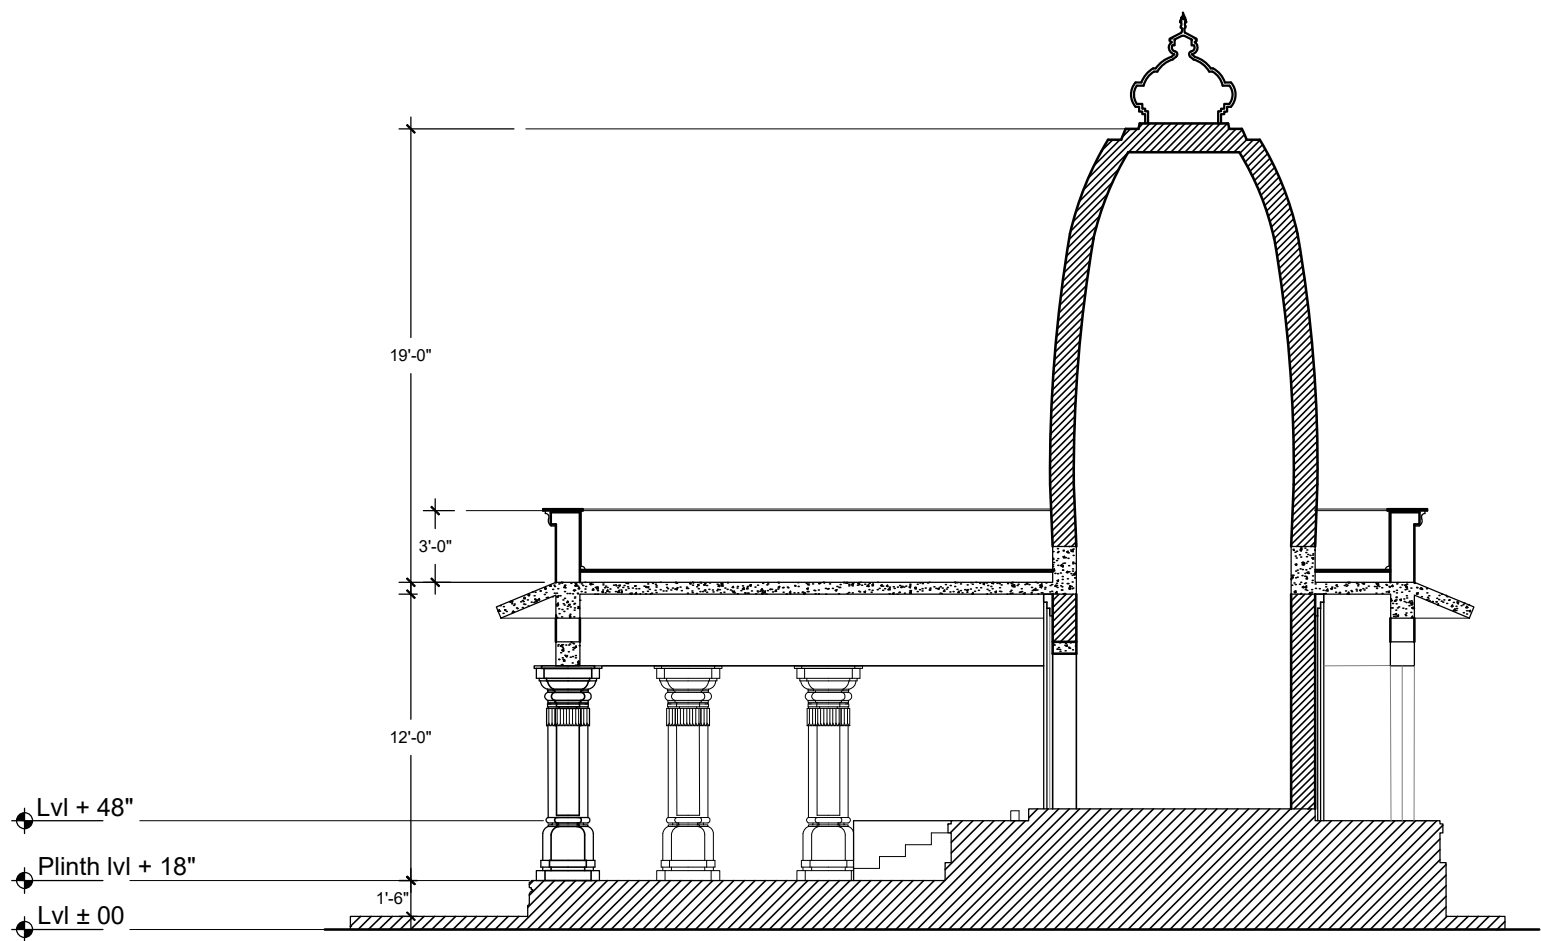

Section AA



Reference image for temple entrance





Reference image for Gopuram




Schematic View

REVISIONS			This drawing is the property of Pradeep Sachdeva Design Associates and may not be used without written consent. Do not scale off this drawing, use figured dimensions only. Verify all dimensions at site.	ARCHITECT PRADEEP SACHDEVA DESIGN ASSOCIATES 4,Windmill Place, Ayanagar Village, New Delhi 110047 Ph:(011)26503741/ 9810054675 , e mail : design@ayanagar.com	PROJECT TEMPLE IN ORISSA		TITLE : Section and Reference images with schematic view	SHEET NO.	
Date	No	Descriptions					DATE : 9-10-2025		Revision no.
							Scale : 1"=8'-0"		

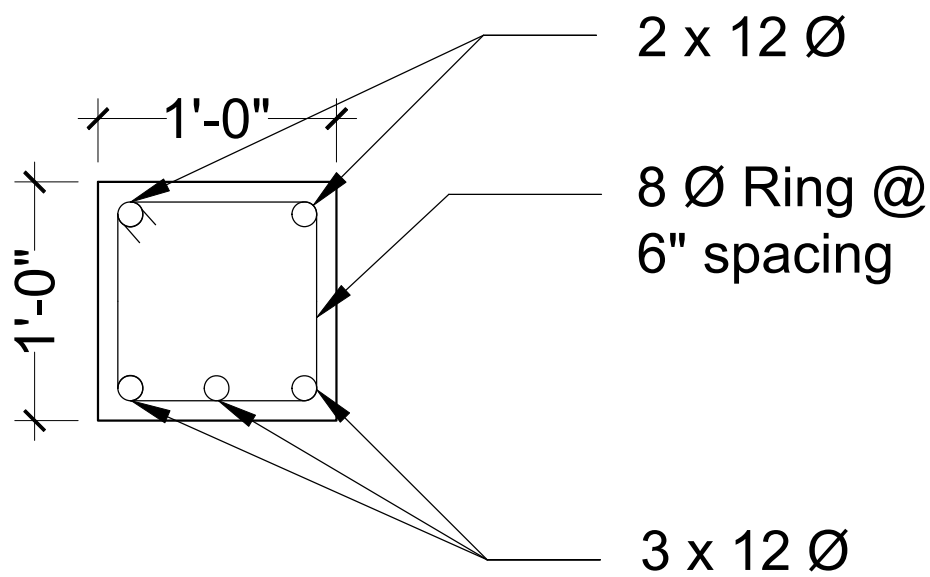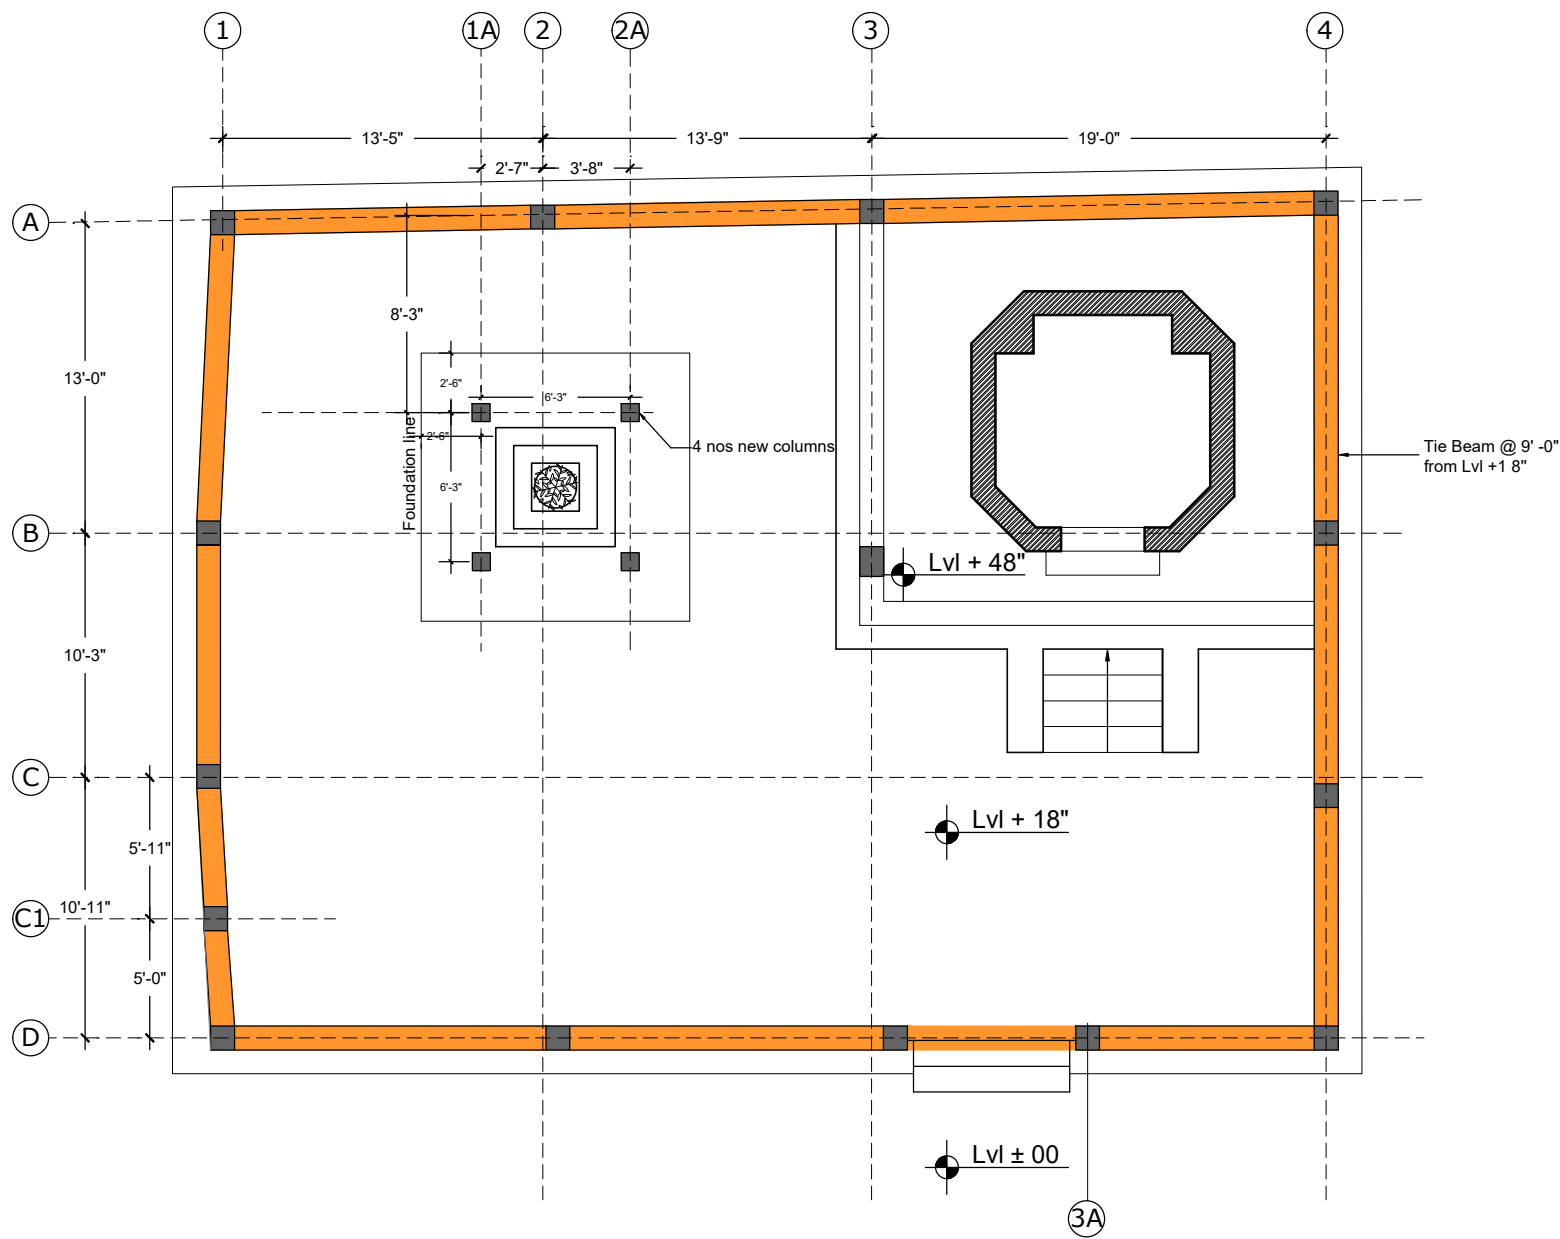


Tie Beam Detail

REVISIONS			This drawing is the property of Pradeep Sachdeva Design Associates and may not be used without written consent. Do not scale off this drawing, use figured dimensions only. Verify all dimensions at site.	ARCHITECT PRADEEP SACHDEVA DESIGN ASSOCIATES 4, Windmill Place, Ayanagar Village, New Delhi 110047 Ph: (011) 26503741 / 9810054675, e mail : design@ayanagar.com	PROJECT TEMPLE IN ORISSA CLIENT	TITLE : Lintel beam detail for periphery wall DATE : 5-11-2025 Scale : 1"=8'-0"	SHEET NO. Revision no.
Date	No	Descriptions					

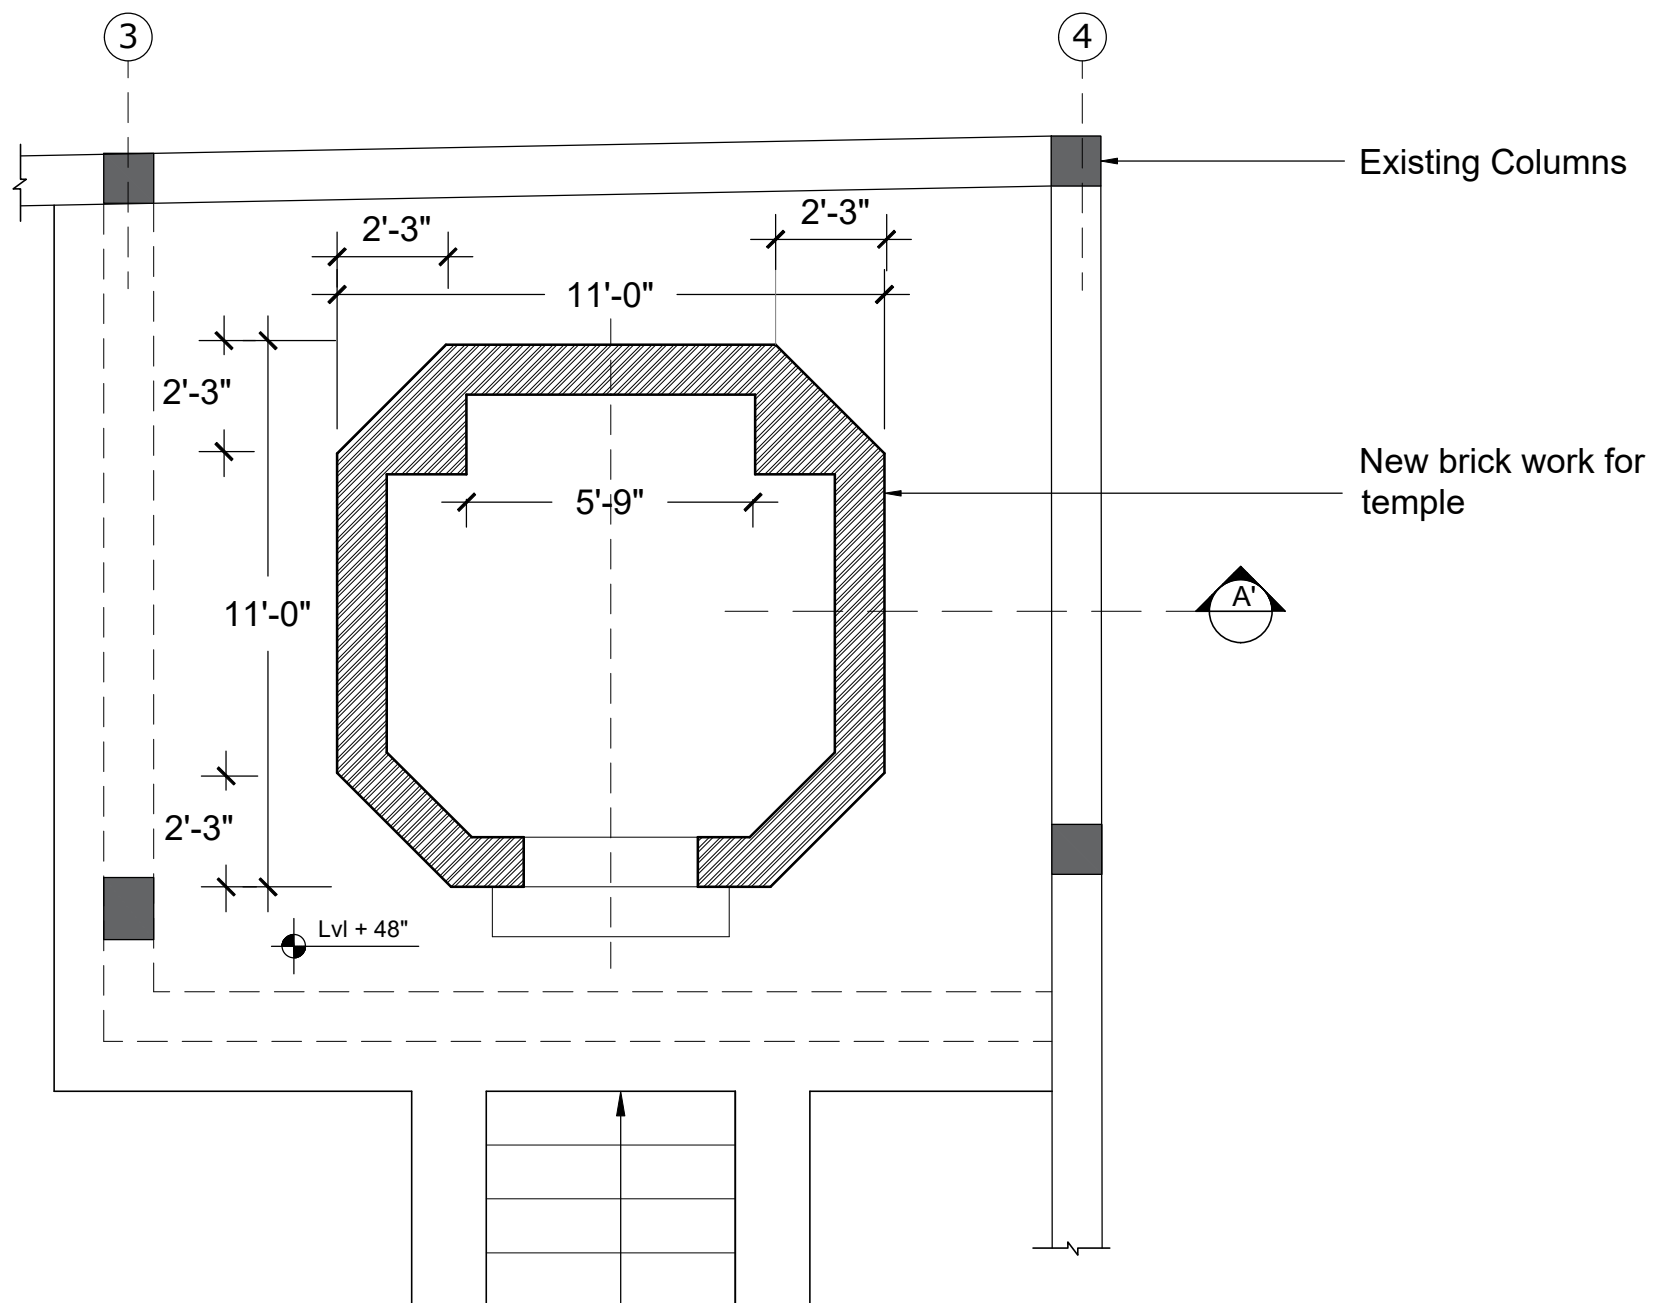


Plan


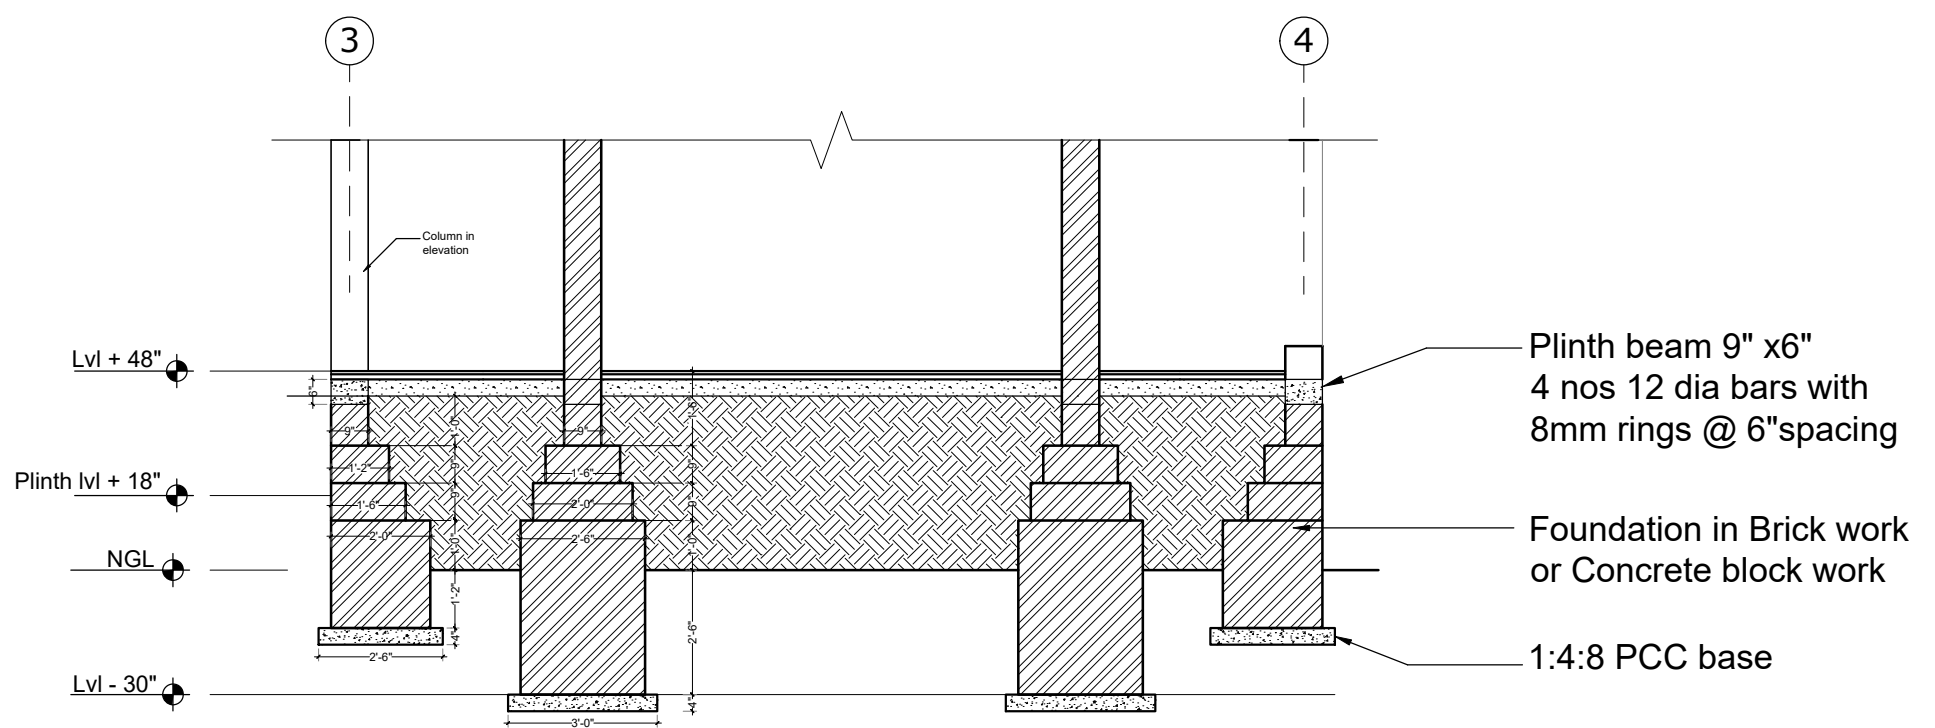


Section A'


REVISIONS			This drawing is the property of Pradeep Sachdeva Design Associates and may not be used without written consent. Do not scale off this drawing, use figured dimensions only. Verify all dimensions at site .	ARCHITECT PRADEEP SACHDEVA DESIGN ASSOCIATES 4, Windmill Place, Ayanagar Village, New Delhi 110047 Ph: (011)26503741/ 9810054675 , e mail : design@ayanagar.com	PROJECT TEMPLE IN ORISSA	TITLE : Plinth and foundation for Temple area	SHEET NO. _____			
Date	No	Descriptions						CLIENT	DATE : 5-11-2025	Revision no. _____

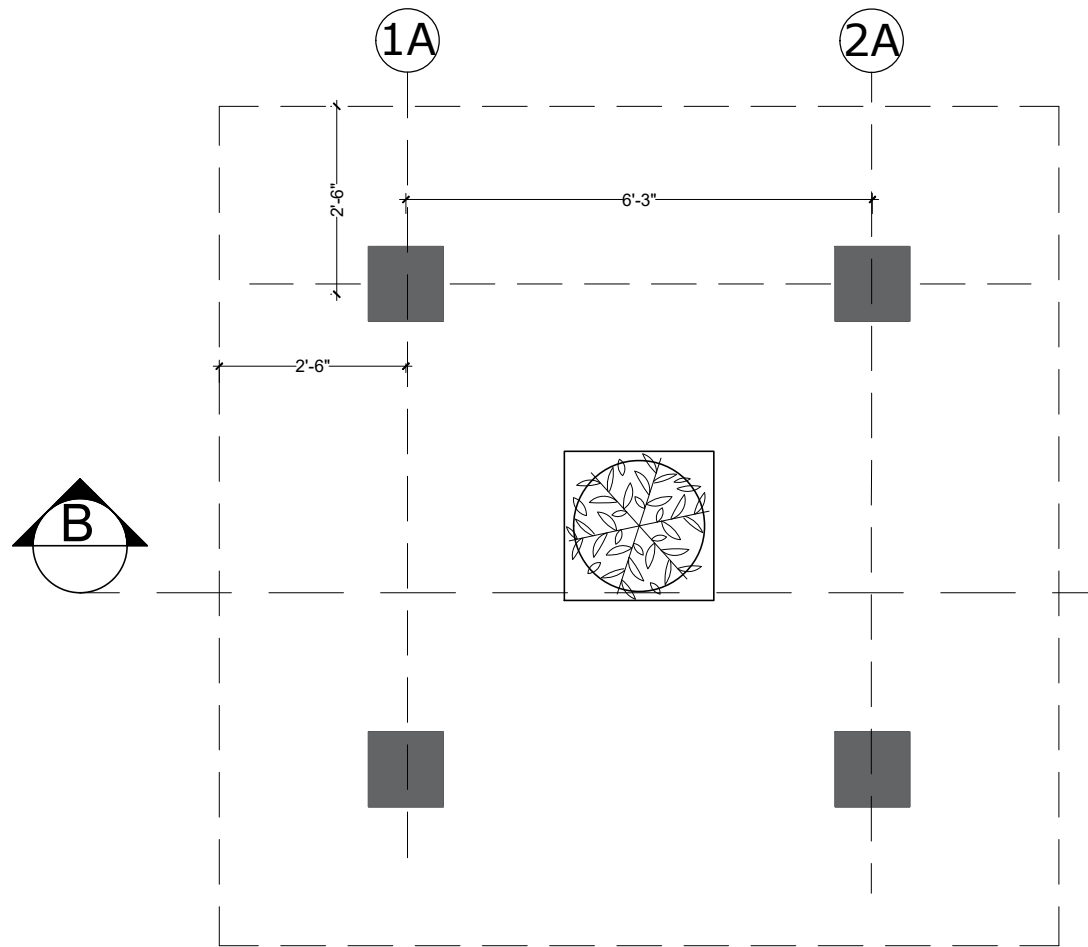

Plan

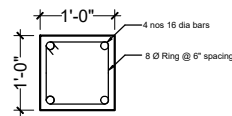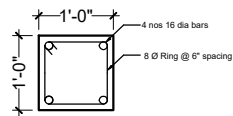

Column detail

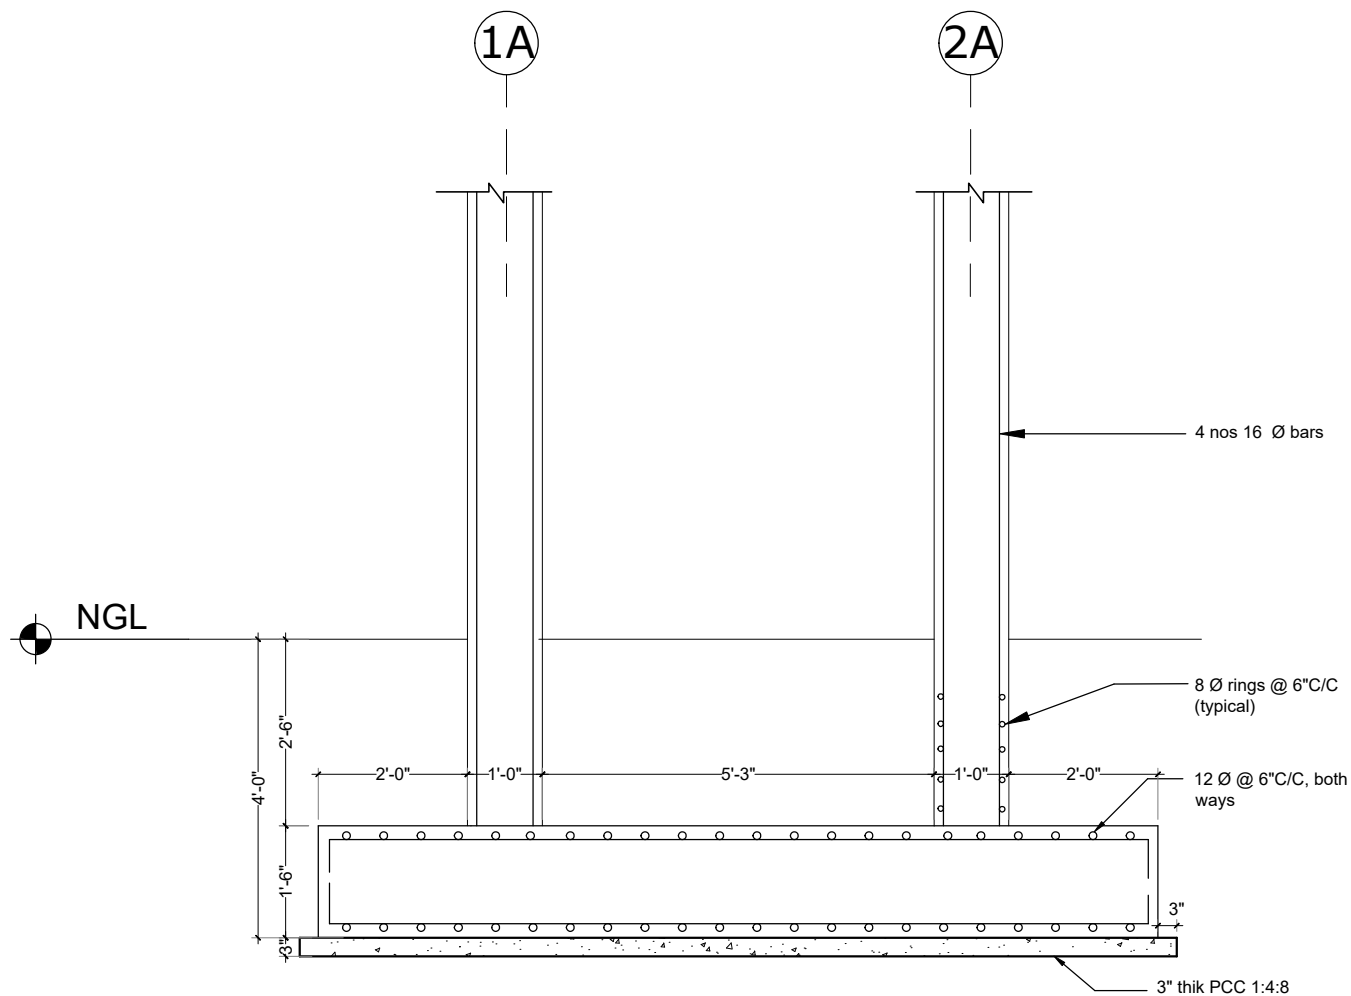

Section B

REVISIONS			This drawing is the property of Pradeep Sachdeva Design Associates and may not be used without written consent. Do not scale off this drawing. use figured dimensions only. Verify all dimensions at site.	ARCHITECT PRADEEP SACHDEVA DESIGN ASSOCIATES 4, Windmill Place, Ayanagar Village, New Delhi 110047 Ph: (011) 26503741 / 9810054675, e mail : design@ayanagar.com	PROJECT TEMPLE IN ORISSA	TITLE : New column details	SHEET NO.
Date	No	Descriptions					
					CLIENT	DATE : 5-11-2025	Revision no.
						Scale : 3"=4'-0" (A3)	